


NOMOGRAMA DE TUBERÍAS  
PVC (n = 0.009) • Manning • Tirante d/D = 0.81 • Ø18"-36"

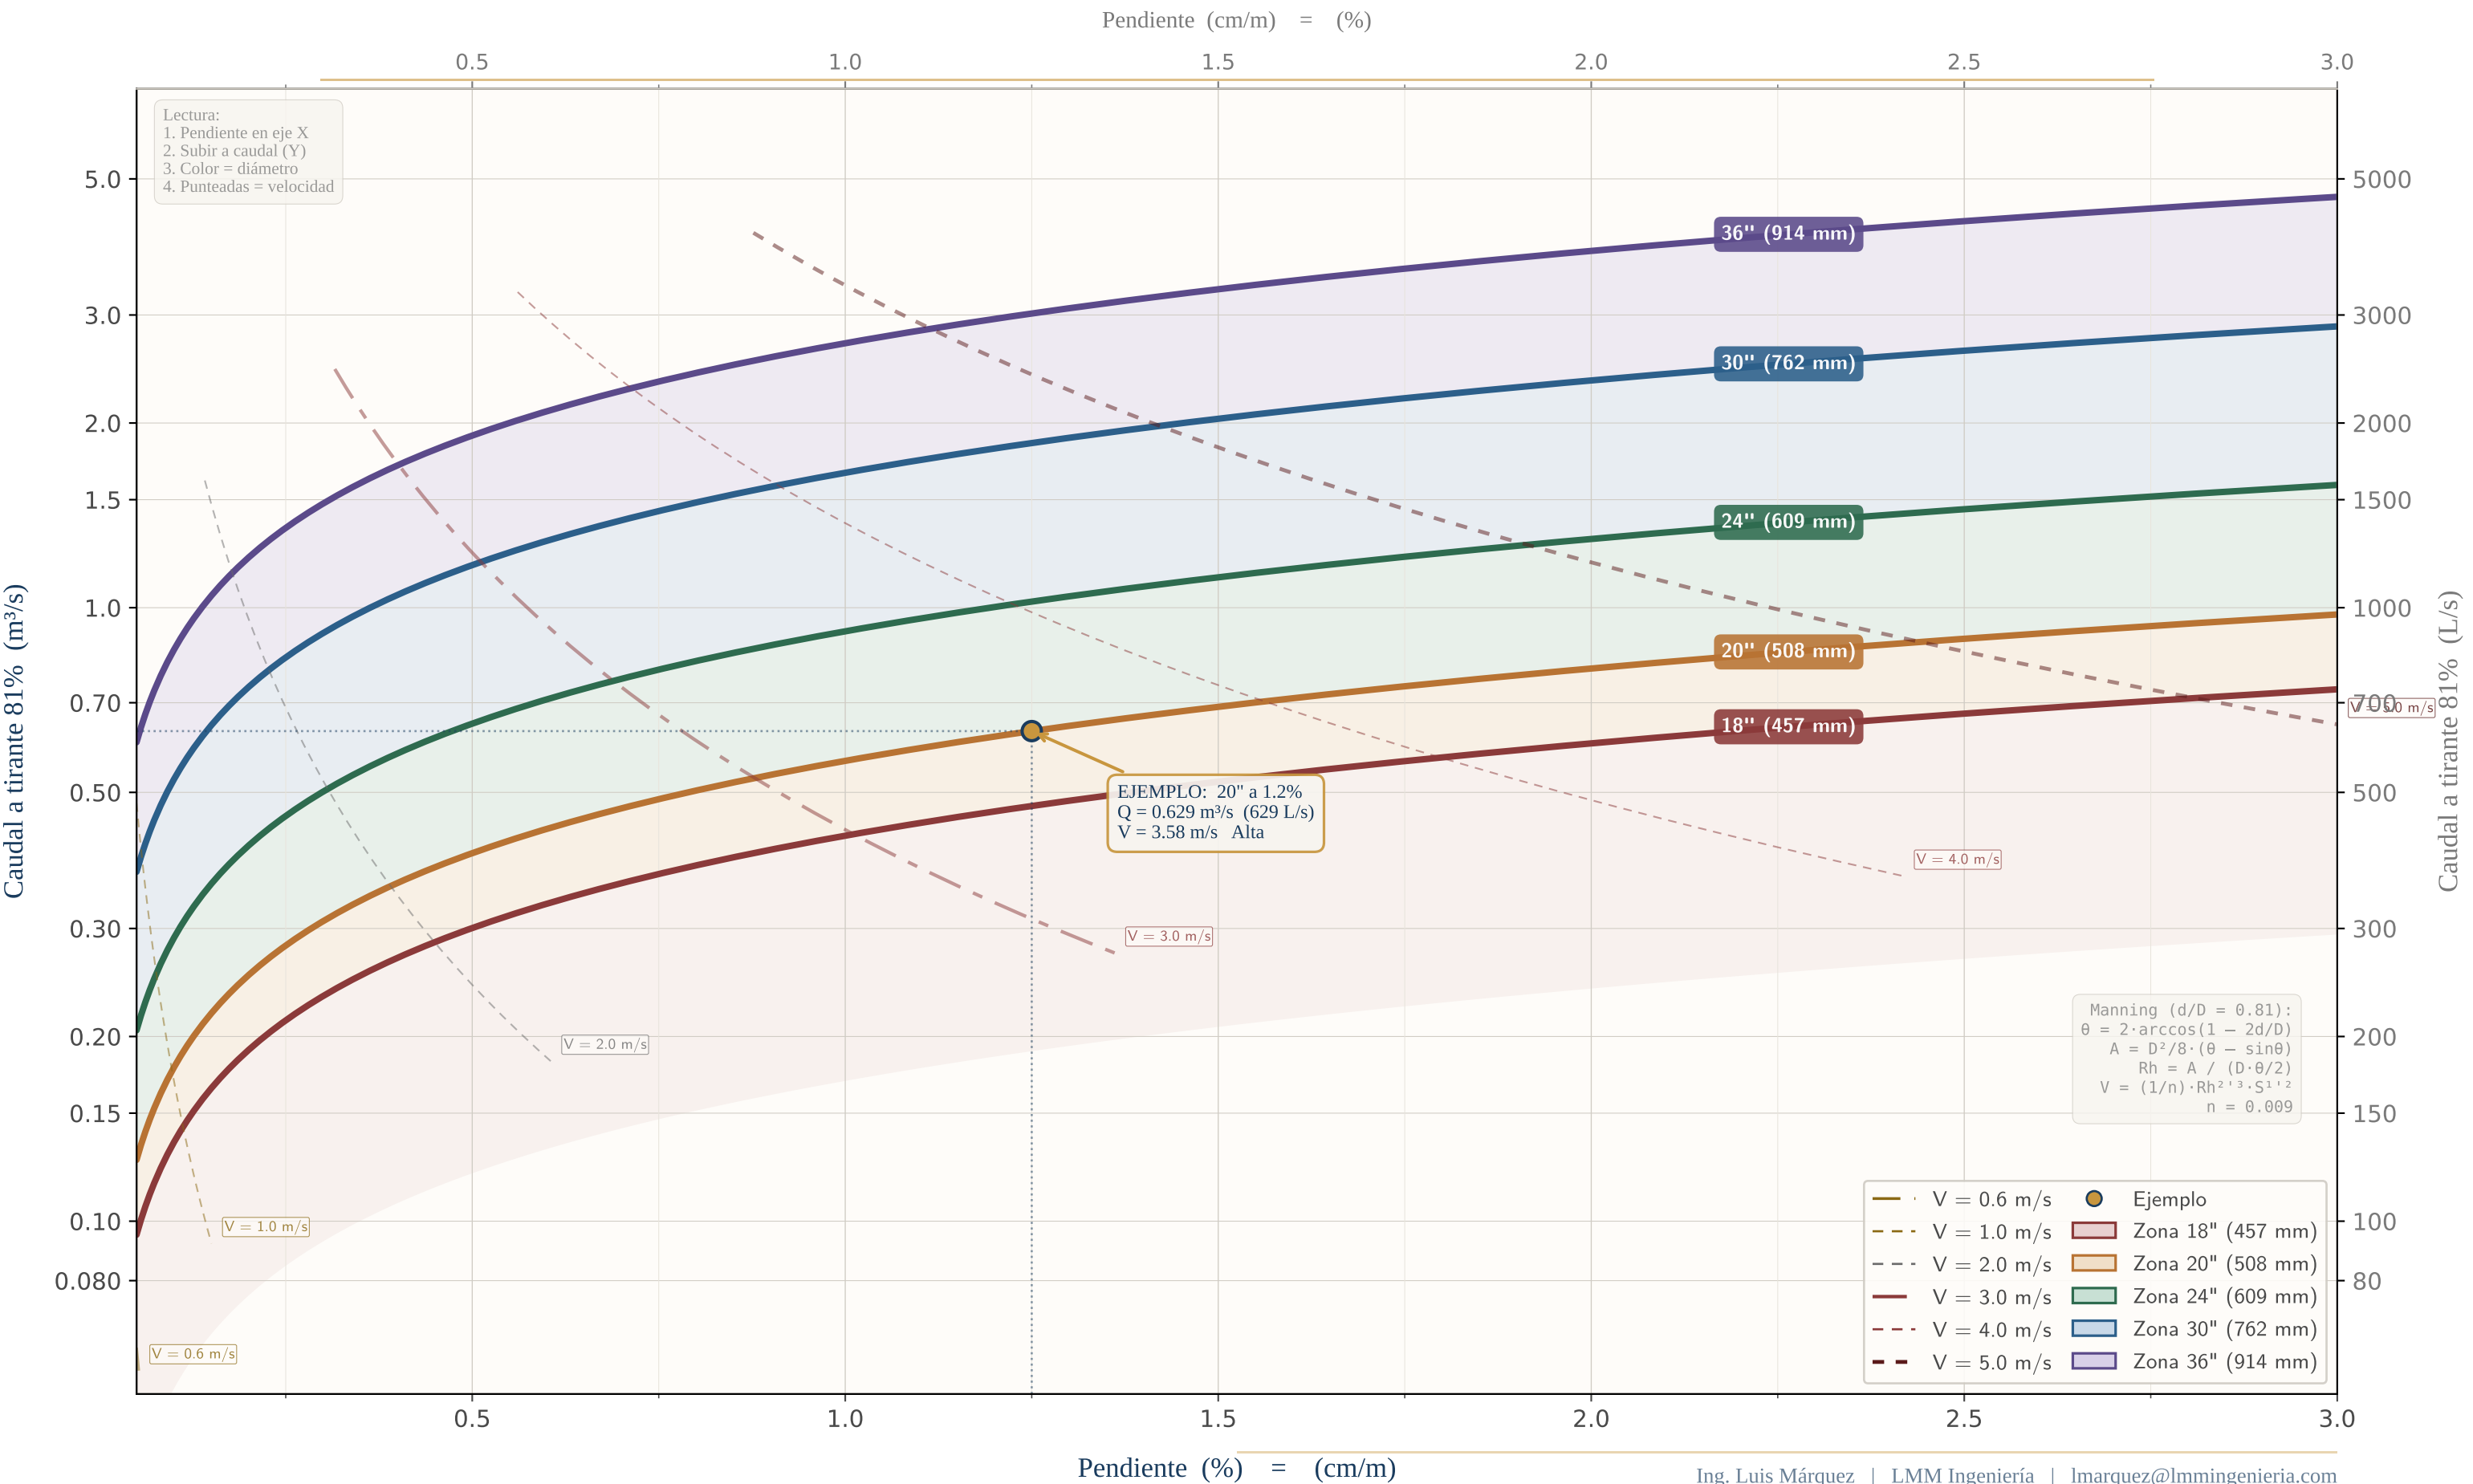

NOMOGRAMA DE TUBERÍAS  
Concreto (n = 0.013) • Manning • Tirante d/D = 0.81 • Ø18"-36"

